All sizes in INCHES · heights above hall floor (+0), platform top 5 3/8" · from MSIL_Set_Build_Dimensions_INCHES.pdf (model 15 Oct 2026) · supersedes earlier poster sizes

ID	Item	Qty	Visible print W × H	Frame / surround	Print file size incl. bleed*	Ratio W:H	Bottom → top above hall floor	Placement	Finish	File @100 ppi (px)
A · Interior wall banners — backlit prints in brass frames										
A1	**Left wall banner 1**	1	**102 3/8" × 102 3/8"**	105 1/8 × 105 1/8 frame	104 3/8" × 104 3/8"	1.000	26" → 128 3/8"	Left wall, y 203 7/8"–306 1/4" from stall front · see W1	Backlit print	10,438 × 10,438
A2	**Left wall banner 2**	1	**102 3/8" × 102 3/8"**	105 1/8 × 105 1/8 frame	104 3/8" × 104 3/8"	1.000	26" → 128 3/8"	Left wall, y 333 7/8"–436 1/4"	Backlit print	10,438 × 10,438
A3	**Left wall banner 3**	1	**102 3/8" × 102 3/8"**	105 1/8 × 105 1/8 frame	104 3/8" × 104 3/8"	1.000	26" → 128 3/8"	Left wall, y 463 3/4"–566 1/8"	Backlit print	10,438 × 10,438
A4	**Right wall banner 1**	1	**102 3/8" × 102 3/8"**	105 1/8 × 105 1/8 frame	104 3/8" × 104 3/8"	1.000	26" → 128 3/8"	Right wall, y 203 7/8"–306 1/4" · see W2	Backlit print	10,438 × 10,438
A5	**Right wall banner 2**	1	**102 3/8" × 102 3/8"**	105 1/8 × 105 1/8 frame	104 3/8" × 104 3/8"	1.000	26" → 128 3/8"	Right wall, y 333 7/8"–436 1/4"	Backlit print	10,438 × 10,438
A6	**Right wall banner 3**	1	**102 3/8" × 102 3/8"**	105 1/8 × 105 1/8 frame	104 3/8" × 104 3/8"	1.000	26" → 128 3/8"	Right wall, y 463 3/4"–566 1/8"	Backlit print	10,438 × 10,438
A7	**Rear wall banner 1**	1	**79 1/2" × 99 5/8"**	82 1/4 × 102 3/8 frame	81 1/2" × 101 5/8"	0.798	31 1/8" → 130 3/4"	Rear wall, x 83 1/8"–3 1/2" left of CL · see W3	Backlit print	8,150 × 10,162
A8	**Rear wall banner 2**	1	**79 1/2" × 99 5/8"**	82 1/4 × 102 3/8 frame	81 1/2" × 101 5/8"	0.798	31 1/8" → 130 3/4"	Rear wall, x 4 3/8"–83 7/8" right of CL	Backlit print	8,150 × 10,162
A9	**Backdrop banner 1 (interior face)**	1	**84" × 72"**	86 3/4 × 74 3/4 frame	86" × 74"	1.167	16 5/8" → 88 5/8"	Backdrop, x 98 3/8"–14 3/8" left of CL · see W4	Backlit print	8,600 × 7,400
A10	**Backdrop banner 2 (interior face)**	1	**84" × 72"**	86 3/4 × 74 3/4 frame	86" × 74"	1.167	16 5/8" → 88 5/8"	Backdrop, x 14 3/8"–98 3/8" right of CL	Backlit print	8,600 × 7,400
C · Frontage — header board, cloth band, side panels, portraits										
C1	**Frontage header board**	1	**575 7/8" × 48"**	—	577 7/8" × 50"	11.997	174 1/2" → 222 1/2"	156 5/8" ahead of stall front; centred on CL · see G3	Printed board	57,788 × 5,000
C2	**Frontage cloth band**	1	**575 7/8" × 30"**	—	577 7/8" × 32"	19.196	144 1/2" → 174 1/2"	Directly below the header board	Printed cloth	57,788 × 3,200
C3	**Left side panel (true face)**	1	**108" × 139 3/4"**	plan width 102 5/8	110" × 141 3/4"	0.773	4 3/4" → 144 1/2"	Raked 18° off the board line · see G3/G4	Printed board	11,000 × 14,175
C4	**Right side panel (true face)**	1	**108" × 139 3/4"**	plan width 99 1/4	110" × 141 3/4"	0.773	4 3/4" → 144 1/2"	Raked 23° off the board line · see G3/G4	Printed board	11,000 × 14,175
C5	**Minister portrait photo**	4	**20 3/8" × 30 1/2"**	24 × 34 1/8 brass frame	21 3/8" × 31 1/2"	0.668	185 3/8" → 215 7/8"	On header board; frame centres 22 1/2" and 66 7/8" each side of CL	Photo print	2,138 × 3,150

28 printed pieces (A–C) + 5 logos/signs (D). *Print file size = visible print + bleed each side: framed banners and boards 1", display prints, portrait photos and canvas 1/2", logos are vector cut-to-shape. Bleed values are a recommendation — confirm with the printer/fabricator. Keep text and logos at least 2" inside the visible edge on banners and boards, 1" on display prints.

P1 · Graphics schedule (1/2) — wall banners and frontage


All sizes in INCHES · heights above hall floor (+0), platform top 5 3/8" · from MSIL_Set_Build_Dimensions_INCHES.pdf (model 15 Oct 2026) · supersedes earlier poster sizes

ID	Item	Qty	Visible print W × H	Frame / surround	Print file size incl. bleed*	Ratio W:H	Bottom → top above hall floor	Placement	Finish	File @100 ppi (px)
B · Showroom graphics — front displays and backdrop (showroom face)										
B1	Stationery hero print	1	36 3/4" × 68 1/4"	in surround 43 5/8 × 93 3/4	37 3/4" × 69 1/4"	0.538	25 5/8" → 94"	Stationery display, front left	Backlit / printed	3,775 × 6,925
B2	Stationery pedestal print	1	36 3/8" × 15 3/4"	plinth 40 5/8 × 19 5/8 high	37 3/8" × 16 3/4"	2.310	7 7/8" → 23 5/8"	Front of stationery plinth	Backlit / printed	3,738 × 1,675
B3	Divisions information panel	1	30 5/8" × 61"	in pylon 37 1/2 × 67 5/8	31 5/8" × 62"	0.502	40 3/4" → 101 3/4"	Divisions pylon, on the centre line	Backlit / printed	3,162 × 6,200
B4	Solar campaign print	1	32 7/8" × 41 3/8"	in surround 41 1/8 × 98	33 7/8" × 42 3/8"	0.795	57" → 98 1/4"	Solar display, front right	Backlit / printed	3,388 × 4,238
B5	Chit Funds campaign print	1	32 7/8" × 83 1/8"	in surround 39 3/8 × 94	33 7/8" × 84 1/8"	0.395	22 1/8" → 105 1/8"	Chit Funds display, front right end	Backlit / printed	3,388 × 8,412
B6	Serving Karnataka panel	1	28 1/8" × 65 1/8"	—	29 1/8" × 66 1/8"	0.432	27 1/8" → 92 1/8"	Between the pylon and the solar display (G2)	Backlit / printed	2,912 × 6,612
B7	Product collage	1	49 1/4" × 36 1/8"	—	50 1/4" × 37 1/8"	1.363	48 3/4" → 84 7/8"	Backdrop showroom face, left of the pylon (G2)	Backlit / printed	5,025 × 3,712
B8	Botanical artwork	3	14 3/4" × 25 1/8"	—	15 3/4" × 26 1/8"	0.587	50 1/8" → 75 1/4"	Backdrop showroom face — 2 left, 1 right (G2)	Canvas print	1,575 × 2,612
D · Logos and exterior signage										
D1	MSIL logo — fascia	1	34 5/8" × 18 7/8"	fascia 346 3/8 × 37	vector, no bleed	1.834	118 1/2" → 137 3/8"	Front fascia, from 19" left of CL (confirm)	Printed / acrylic	—
D2	MSIL logo — reception desk	1	26" × 14 1/8"	desk 69 3/4 wide	vector, no bleed	1.841	15 3/8" → 29 5/8"	Reception desk front, centred (G2)	Printed / acrylic	—
D3	Exterior left wall — MSIL logotype	1	29 7/8" × 9 3/4"	lockup zone 53 7/8 wide	vector, no bleed	3.064	105 7/8" → 115 5/8"	Starts 118 5/8" from stall front · see W5	Printed	—
D4	Exterior left wall — "Everyday Essentials" block	1	44 1/8" × 9 3/4"	—	vector, no bleed	4.526	20" → 29 3/4"	Under the lockup (x not dimensioned) · see W5	Printed	—
D5	Exterior right wall — MSIL logotype	1	29 7/8" × 9 3/4"	lockup zone 53 7/8 wide	vector, no bleed	3.064	105 7/8" → 115 5/8"	Starts 119 1/8" from stall front · see W5	Printed	—

Showroom graphics sit inside their display surrounds; the pack gives heights but not x positions for B6–B8 and D4 — use the G2 reference (sheet P6) and confirm on site. *Print file size = visible print + bleed each side: framed banners and boards 1", display prints, portrait photos and canvas 1/2", logos are vector cut-to-shape. Bleed values are a recommendation — confirm with the printer/fabricator. Keep text and logos at least 2" inside the visible edge on banners and boards, 1" on display prints.

P2 · Graphics schedule (2/2) — showroom graphics, logos and signage


All sizes in INCHES · heights above hall floor (+0), platform top 5 3/8" · from MSIL_Set_Build_Dimensions_INCHES.pdf (model 15 Oct 2026) · supersedes earlier poster sizes

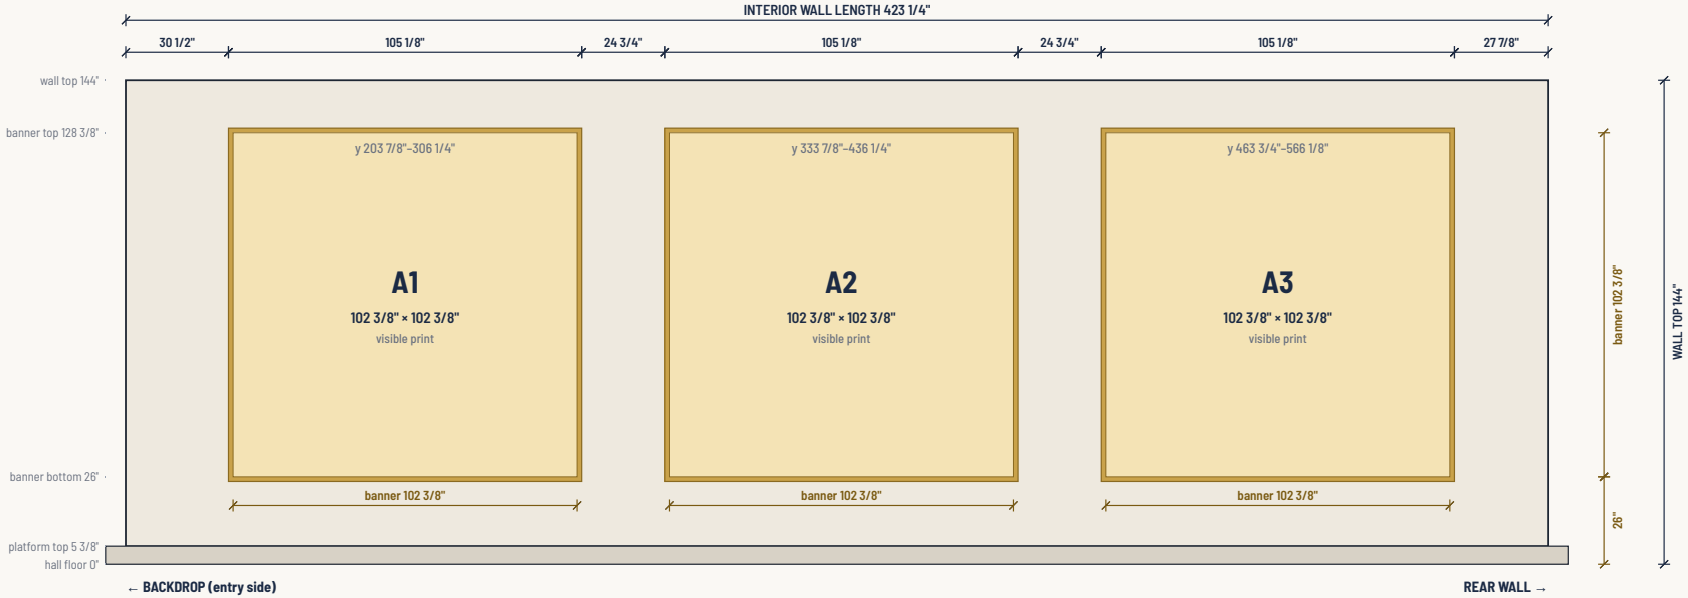

3 banners, each 102 3/8" × 102 3/8" visible, in brass frames 105 1/8" × 105 1/8" (1 3/8" lip). Banner bottom 26", top 128 3/8" above hall floor (20 5/8"–123" above platform). First frame 30 1/2" from the backdrop, frames 24 3/4" apart, last frame 27 3/4" from the rear wall. y = distance from the stall front edge.

P3 · Left wall — interior face, banners A1–A3 (entry at the left)

All sizes in INCHES · heights above hall floor (+0), platform top 5 3/8" · from MSIL_Set_Build_Dimensions_INCHES.pdf (model 15 Oct 2026) · supersedes earlier poster sizes

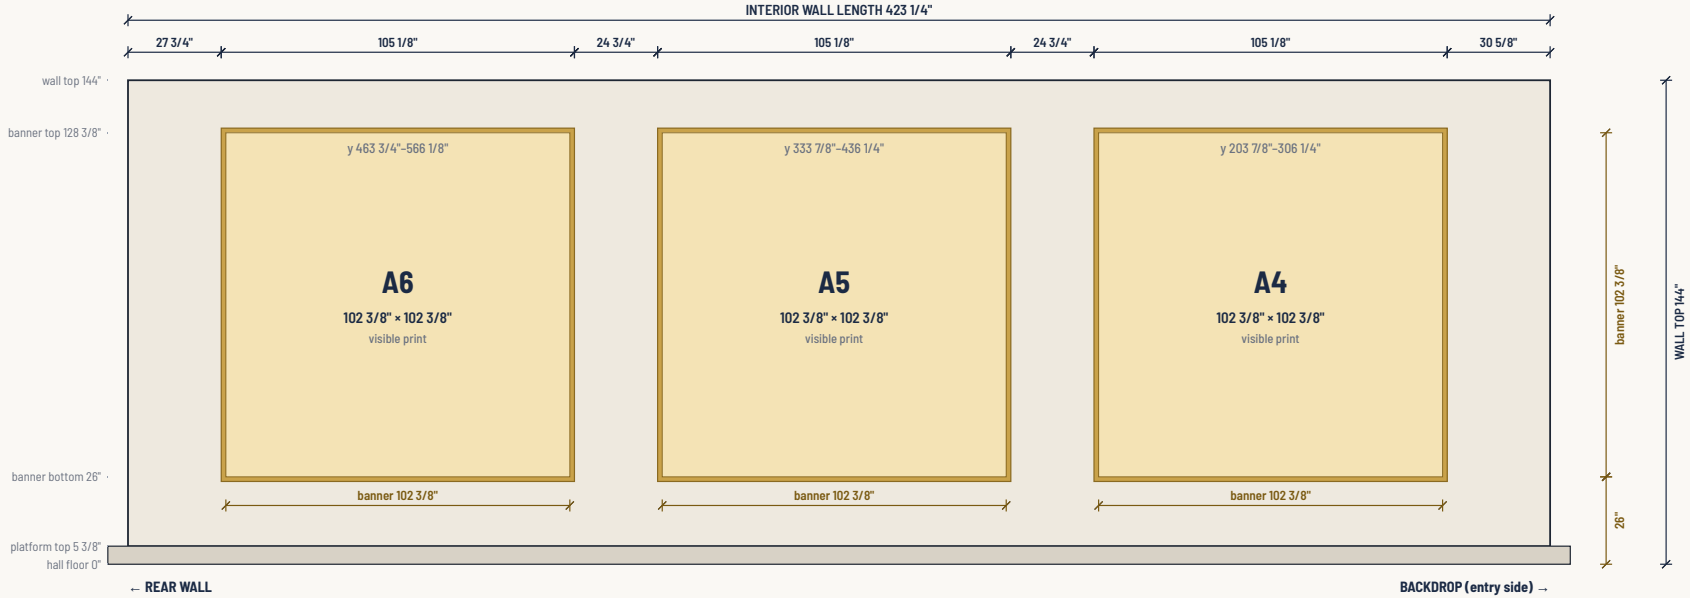


3 banners, each 102 3/8" × 102 3/8" visible, same sizes and heights as the left wall, mirrored: A4 is nearest the backdrop. Frame 105 1/8" × 105 1/8"; banner bottom 26", top 128 3/8".

P4 · Right wall — interior face, banners A4–A6 (entry at the right)

All sizes in INCHES · heights above hall floor (+0), platform top 5 3/8" · from MSIL_Set_Build_Dimensions_INCHES.pdf (model 15 Oct 2026) · supersedes earlier poster sizes



REAR WALL — interior face (looking at the rear wall; stall-left on the left)

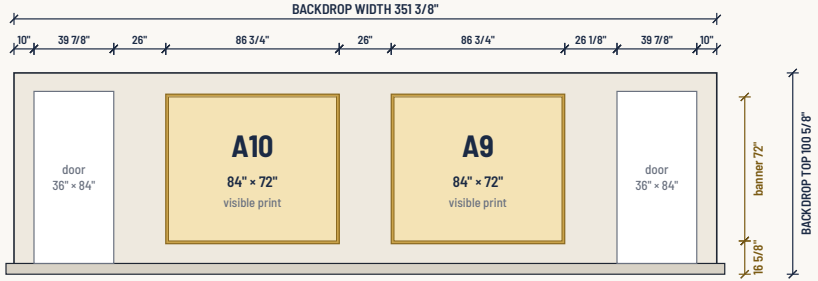


BACKDROP — interior face (looking toward the entry; stall-left on the right)

Rear wall: 2 banners 79 1/2" × 99 5/8" visible (frames 82 1/4" × 102 3/8"), bottom 31 1/8", top 130 3/4"; frames 5 1/8" apart. **Backdrop interior: 2 banners 84" × 72" visible** (frames 86 3/4" × 74 3/4"), bottom 16 5/8", top 88 5/8"; frames 26" apart, between the two 36" × 84" doors. Backdrop banner 1 (A9) is on the stall-left side, which appears on the right when facing the entry.

P5 · Rear wall (A7–A8) and backdrop interior face (A9–A10)

All sizes in INCHES · heights above hall floor (+0), platform top 5 3/8" · from MSIL_Set_Build_Dimensions_INCHES.pdf (model 15 Oct 2026) · supersedes earlier poster sizes

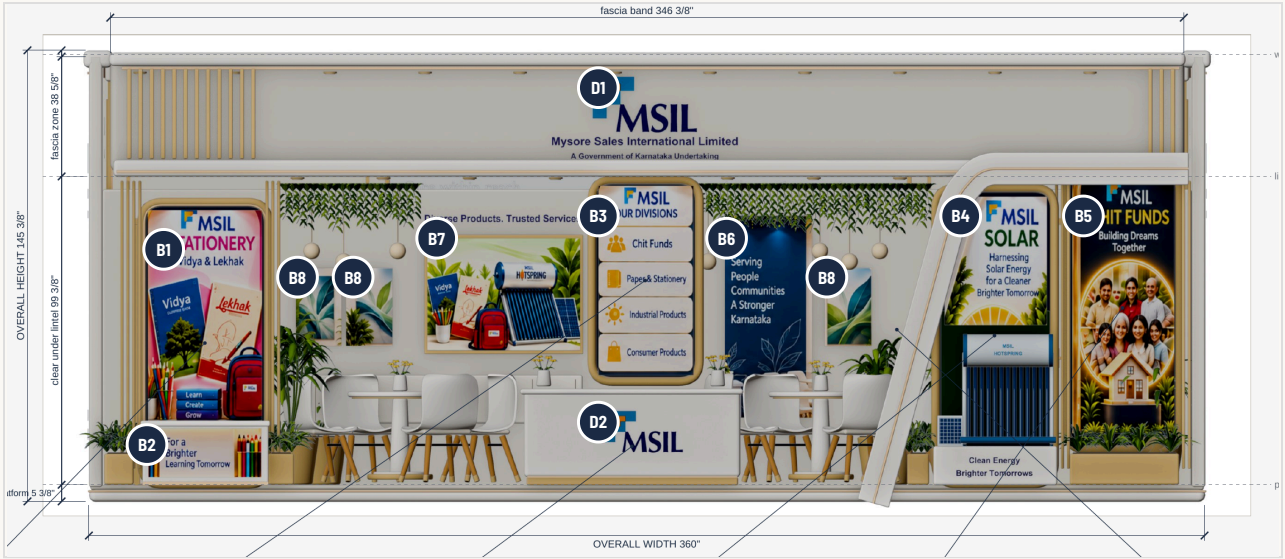

B1 Stationery hero print — 36 3/4" × 68 1/4", 25 5/8" → 94"

B2 Stationery pedestal print — 36 3/8" × 15 3/4", 7 7/8" → 23 5/8"

B3 Divisions information panel — 30 5/8" × 61", 40 3/4" → 101 3/4"

B4 Solar campaign print — 32 7/8" × 41 3/8", 57" → 98 1/4"

B5 Chit Funds campaign print — 32 7/8" × 83 1/8", 22 1/8" → 105 1/8"

B6 Serving Karnataka panel — 28 1/8" × 65 1/8", 27 1/8" → 92 1/8"

B7 Product collage — 49 1/4" × 36 1/8", 48 3/4" → 84 7/8"

B8 Botanical artwork — 14 3/4" × 25 1/8" ×3, 50 1/8" → 75 1/4"


D1 MSIL logo — fascia — 34 5/8" × 18 7/8", 118 1/2" → 137 3/8"

D2 MSIL logo — reception desk — 26" × 14 1/8", 15 3/8" → 29 5/8"

Reference image is the G2 render from the set-build pack; tags mark where each graphic sits. Heights are exact (from E2); horizontal positions of B6–B8 are not dimensioned in the pack — set them out from G2 and confirm on site.

P6 · Front of the stall — showroom graphics placement (reference: sheet G2)

All sizes in INCHES · heights above hall floor (+0), platform top 5 3/8" · from MSIL_Set_Build_Dimensions_INCHES.pdf (model 15 Oct 2026) · supersedes earlier poster sizes

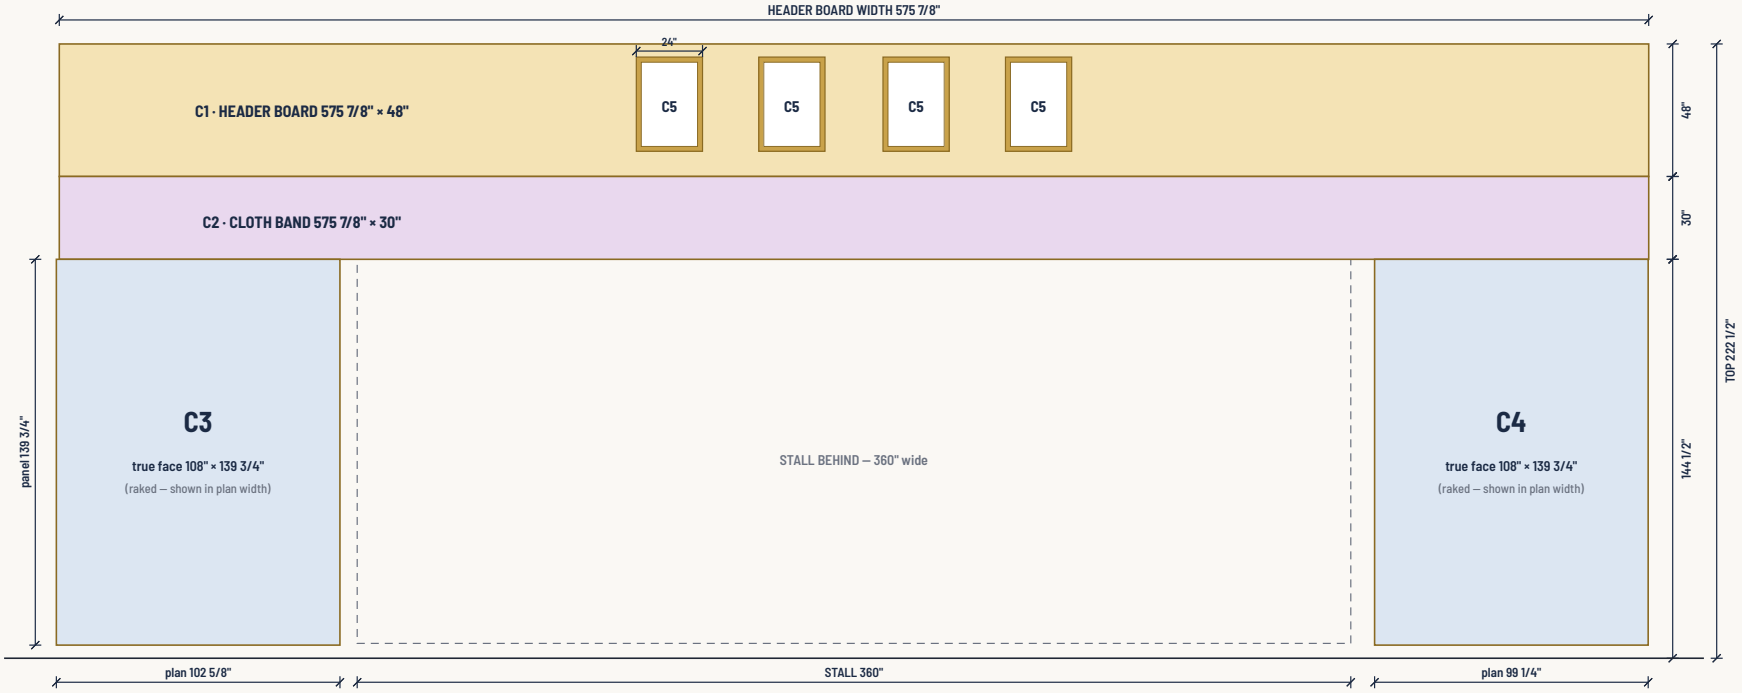


C1 header board 575 7/8" × 48" (174 1/2"–222 1/2") and **C2 cloth band 575 7/8" × 30"** (144 1/2"–174 1/2"), both 156 5/8" in front of the stall and centred on it (107 7/8" overhang each side). **C3/C4 side panels: print the true face 108" × 139 3/4"** (4 3/4"–144 1/2") — the drawing shows their raked plan widths. **C5 portraits ×4:** photo 20 3/8" × 30 1/2" in 24" × 34 1/8" frames, frame bottom 183 5/8", centres 22 1/2" and 66 7/8" each side of the centre line; name line under each.

P7 · Frontage — header board, cloth band, side panels and portraits (front elevation)

All sizes in INCHES · heights above hall floor (+0), platform top 5 3/8" · from MSIL_Set_Build_Dimensions_INCHES.pdf (model 15 Oct 2026) · supersedes earlier poster sizes



LEFT WALL — exterior (front of stall on the right)

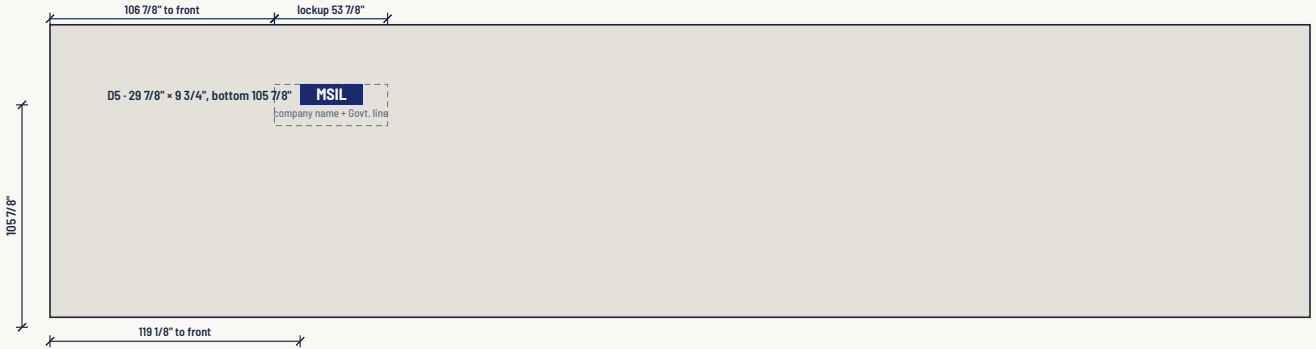

RIGHT WALL — exterior (front of stall on the left)

Each side wall is 600" long, 144" to the wall top. The MSIL logotype sits in a 53 7/8"-wide lockup that starts 106 7/8" from the stall front, with the company name and Government line below it (their heights are not given in the pack — confirm). The "Everyday Essentials for a Brighter Tomorrow" block is on the left wall only, bottom 20"; it is drawn centred under the lockup as on sheet W5 (x not dimensioned). The rear outer face carries no graphics.

P8 · Exterior side walls — signage D3–D5 (seen from outside)

All sizes in INCHES · heights above hall floor (+0), platform top 5 3/8" · from MSIL_Set_Build_Dimensions_INCHES.pdf (model 15 Oct 2026) · supersedes earlier poster sizes

Print files

- Set each Illustrator artboard to the **print file size incl. bleed** (P1–P2). Visible size = trim inside the frame or surround.
- **Header board and cloth band are wider than Illustrator's 227" canvas limit.** Use *New Document › Large canvas* (1:10 scale: board artboard 57 25/32" × 5"), or build at 1:4 and tell the printer the scale.
- Resolution at full size: 100 ppi for banners and showroom prints; 50–75 ppi is enough for the header board, cloth and side panels (viewed from distance); 150 ppi for portrait photos.
- Logos (D1–D5) must be vector. Convert type to outlines or package fonts.
- Backlit prints: supply CMYK with the printer's backlit profile; avoid large flat dark areas.

Confirm before printing

- Bleed per side (1" framed/boards, 1/2" displays) — printer to confirm, incl. pole pockets or hems on the cloth band.
- Fascia logo D1: "19" left of centre line" — start edge or centre?
- Horizontal positions of B6, B7, B8 and D4; heights of the exterior company-name and Government lines.
- Side panels C3/C4 are raked differently (18° and 23°) — artwork is the 108" true face either way.
- Doors in the backdrop are drawn as applied frames; if real openings are cut, A9/A10 positions stay as shown.
- Per the pack: earlier PDFs and poster files were made for an older model (two side posters, not three banners per side wall). Use these sizes.

Fit check — artworks rebuilt in this project

Artwork (ratio)	Nearest slot (ratio)	Fit
Solar Products poster (0.977)	A1–A6 wall banner (1.000)	~2% — re-crop
Heat-pump slides (1.333)	B7 product collage (1.363)	~2% — re-crop
Solar roll-up (0.435)	B6 Serving Karnataka (0.432)	~1% — wrong content
Solar roll-up (0.435)	B5 Chit Funds print (0.396)	~10% — re-layout
Solar Portfolio banner (2.452)	— (B2 pedestal 2.310)	re-layout
Chits backdrop (3.254)	— no slot this shape	re-layout

All rebuilt artworks are far below full-size resolution (e.g. a 102 3/8" banner needs ~10,240 px at 100 ppi); photos must be relinked to high-res originals.